ПРАВИТЕЛЬСТВО МОСКВЫ

КОМИТЕТ ПО АРХИТЕКТУРЕ И ГРАДОСТРОИТЕЛЬСТВУ ГОРОДА МОСКВЫ (МОСКОМАРХИТЕКТУРА)

16. 10. 2019
дата

19/04406
номер

Паспорт колористического решения

фасадов зданий, строений, сооружений в городе Москве

АДРЕС ОБЪЕКТА **Маршала Бирюзова ул., д. 20, корп. 1**

РАЙОН ГОРОДА МОСКВЫ **Щукино**

АДМИНИСТРАТИВНЫЙ ОКРУГ ГОРОДА МОСКВЫ **СЗАО**

И. о. заместителя председателя
(должность уполномоченного должностного лица Москомархитектуры)

(подпись)

Фролова Ю. А.
(расшифровка подписи)

https://moskvakadastr.ru/

I. ОБЩИЕ СВЕДЕНИЯ ОБ ОБЪЕКТЕ

1. **Адрес объекта:** Маршала Бирюзова ул., д. 20, корп. 1.
2. **Наименование объекта:** Встроенно-пристроенное (торговое) помещение к жилому многоквартирному дому.
3. **Правообладатель:** ООО «ВАЛЕНТИНА ПЛЮС».
4. **Год постройки:** 1988.
5. **Этажность:** 1.
6. **Расположение объекта в зоне охраны культурного наследия:**

   - на территории объекта культурного наследия: ___.

   - в границах зоны охраны объекта культурного наследия: зона №

   Согласование с Департаментом культурного наследия города Москвы
   Заключение: не требуется номер: дата:

7. **Вид работ по объекту:** ремонт фасадов, осуществляемый с частичным изменением колористического решения фасадов.
8. **Разработчик проекта:** ИП Валезнев М. А.
   генеральный директор -, архитектор -, тел: -.
9. **СРО:** Ассоциация проектировщиков «Национальное Проектное Объединение» № 72 от 23.08.2018 г.
10. **Особые условия:** Паспорт не дает право на производство работ. Паспорт колористического решения фасадов зданий, строений, сооружений в городе Москве подготовлен по материалам (Проект колористического решения фасадов), предоставленным заказчиком.


https://moskvakadastr.ru/

1. Текстовая часть, содержащая информацию о расположении объекта в структуре города и квартала, морфотипе и колористике застройки и пр. (Подтверждается схемами расположения объекта в структуре города и данными фотофиксации).
Нежилое здание расположено в Северо-Западном административном округе, в районе Щукино, на линии застройки улицы Маршала Бирюзова. Ближайшая магистраль - улица Народного Ополчения. Ближайшая станция метро - Октябрьское Поле. Окружающая застройка состоит из многоквартирных жилых домов, учебно-научных, административных, общественных зданий. Колористика окружающей застройки - светло-жёлтого, жёлтого, оранжевого, серого цветов.

2. Функциональная территориальная зона (в соответствии с генеральным планом города Москвы):
- зоны жилых микрорайонов и жилых групп многоквартирной жилой застройки.

https://moskvakadastr.ru/

3. Местоположение объекта в структуре города (схема).

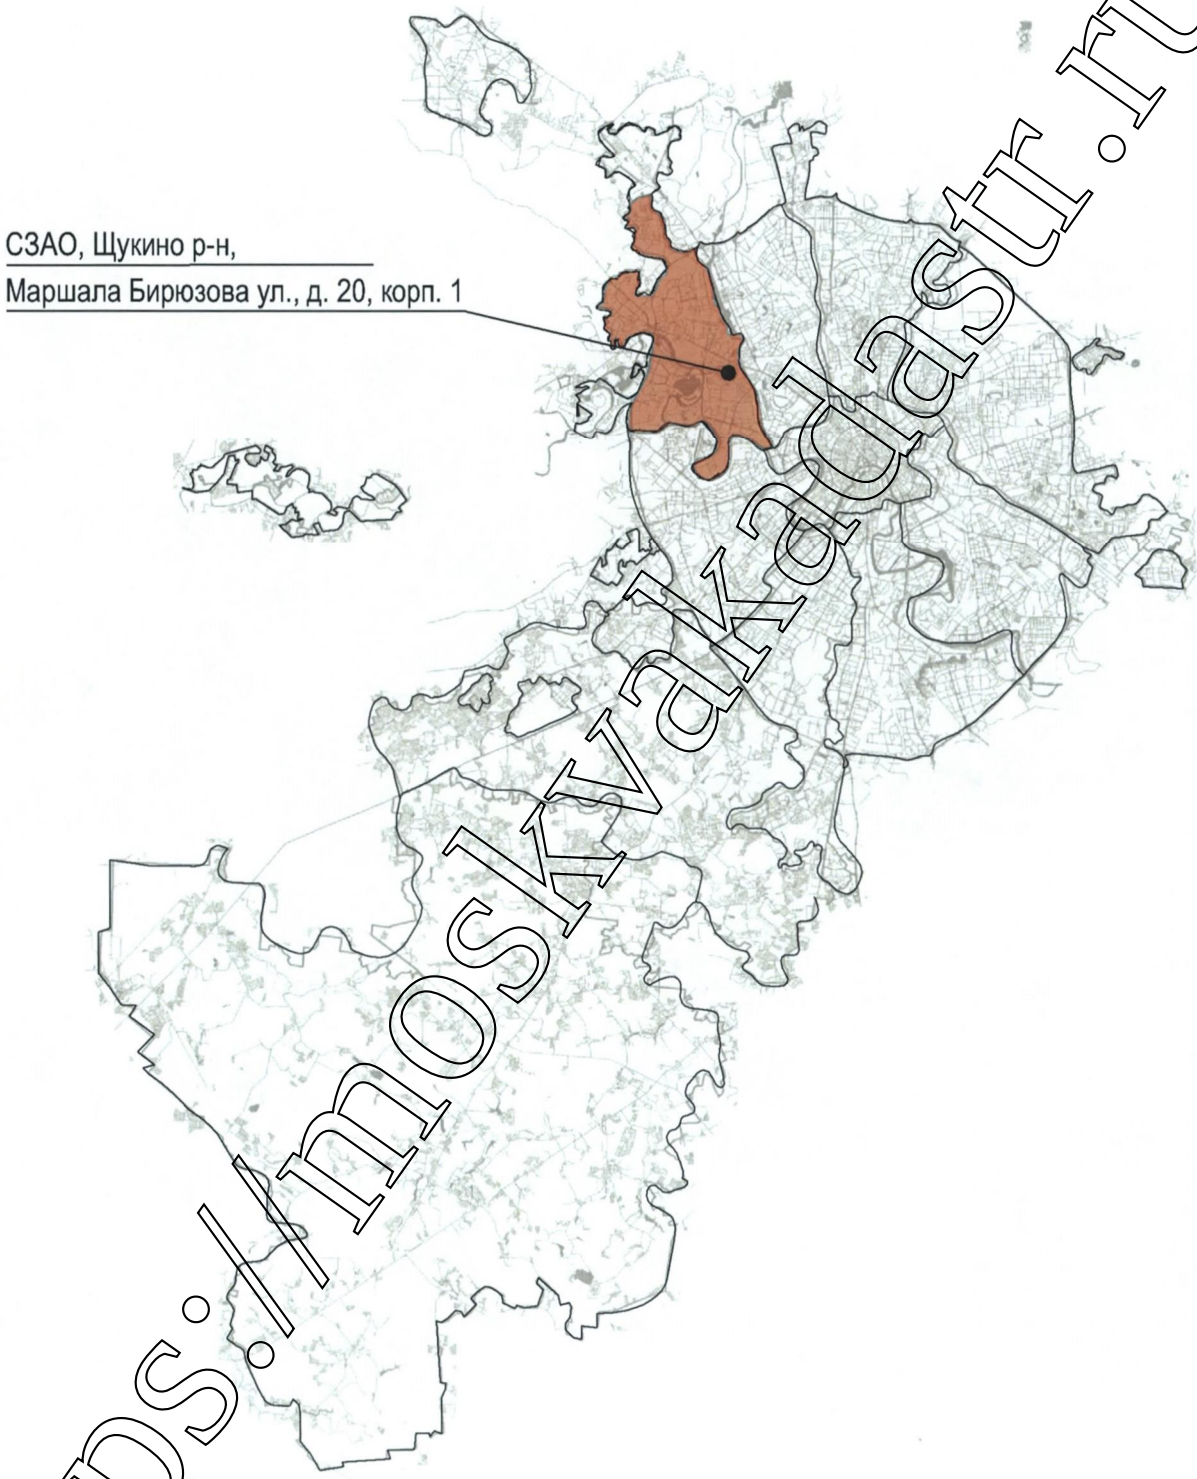


● - рассматриваемый объект

■ - расположение здание в структуре города

https://moskvakadastr.ru/

4. Местоположение объекта в структуре квартала

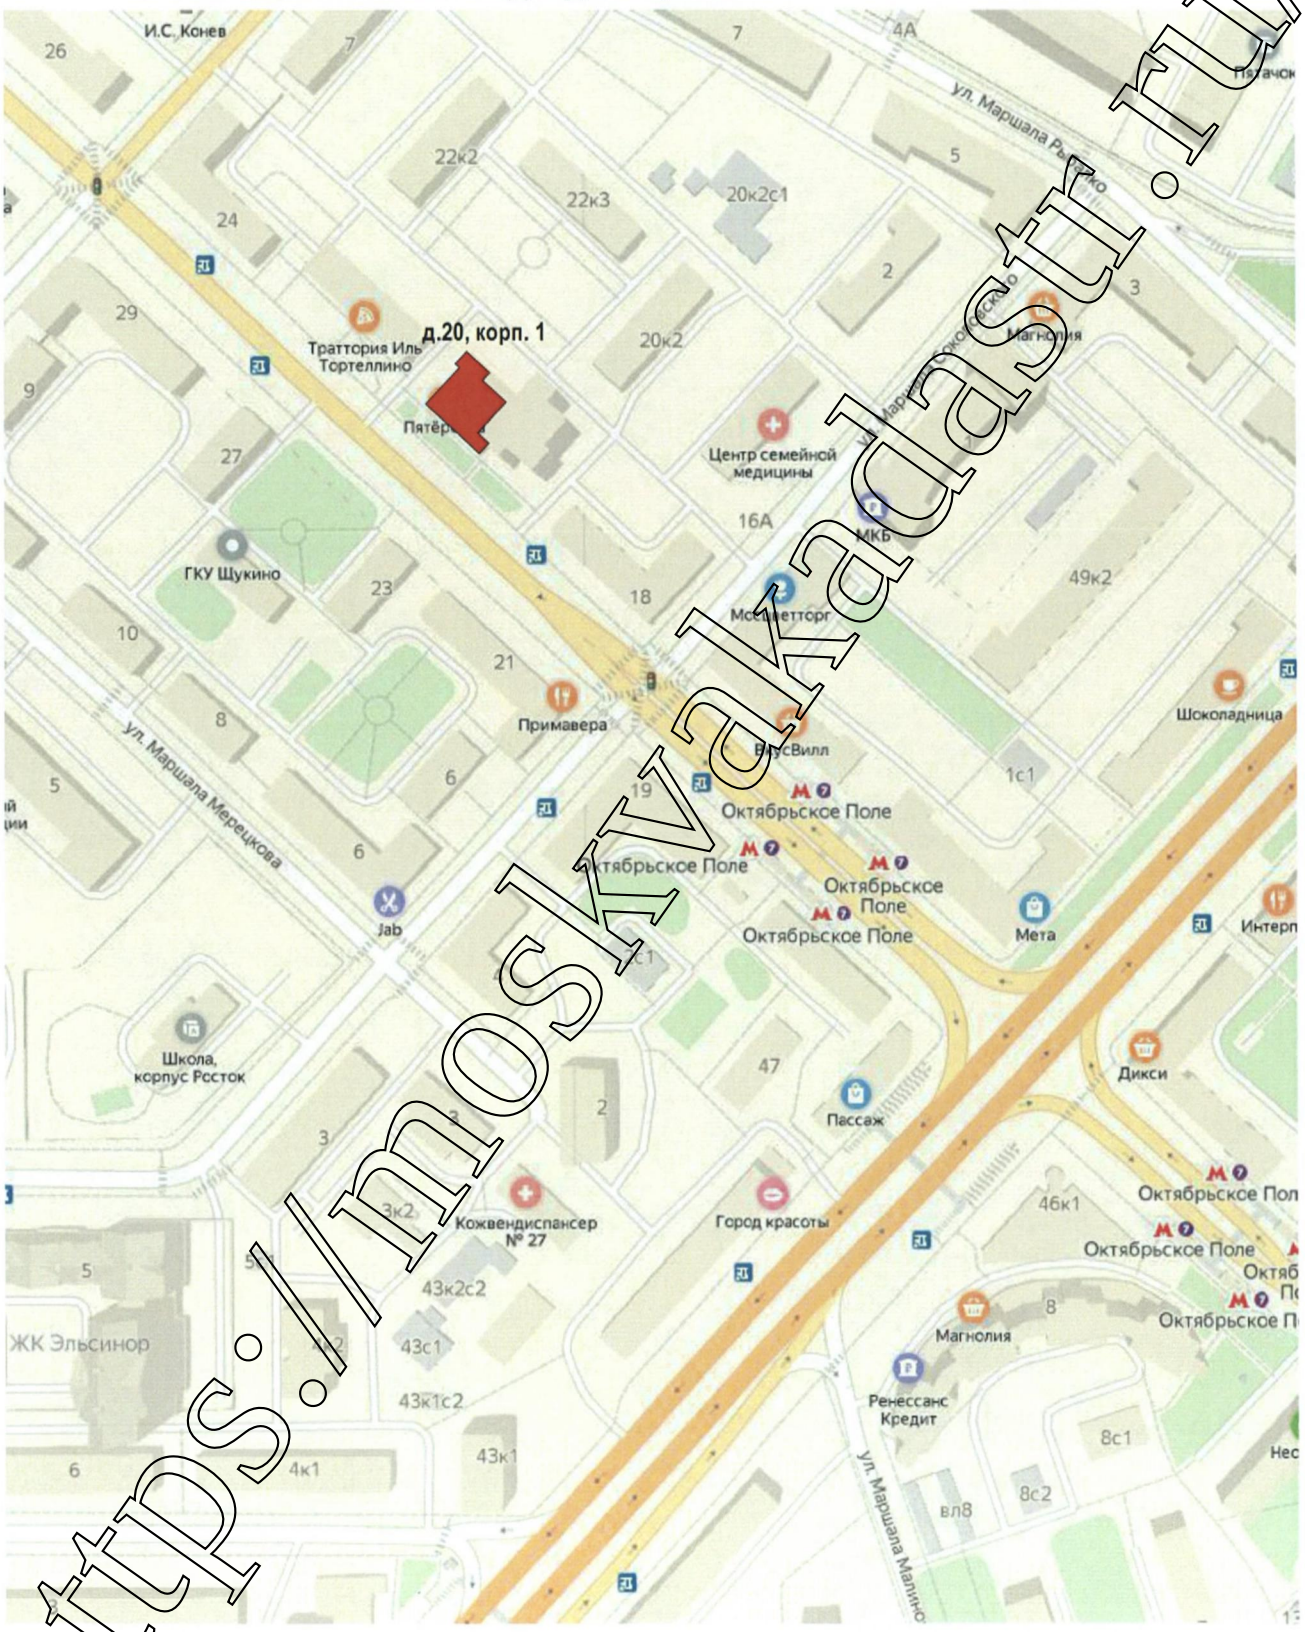

- рассматриваемое здание

https://moskvakadastr.ru/


5. Фотофиксация окружающей застройки (среды)

ВИД.1



ВИД.2



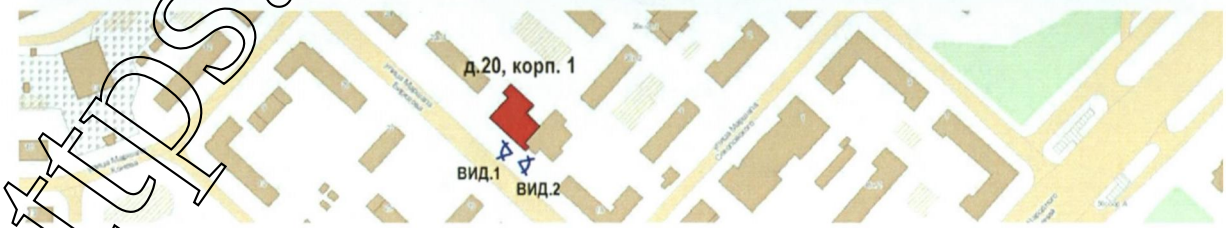

- рассматриваемое здание

Вид 1 - точки съемки

https://moskvakadastr.ru/

1. Текстовая часть, содержащая информацию об архитектурной стилистике объекта, пластике фасада, форме здания в плане, колористике, наличии архитектурных деталей на фасаде и пр. (подтверждается материалами фотофиксации)

Объектом проектирования является кирпичный 1-этажный магазин (встроенно-пристроенное помещение в 9-этажный многоквартирный жилой дом), построенный в 1988 году. Объект является зданием, обладающим признаками объекта культурного наследия. Здание прямоугольное в плане. На фасадах присутствуют витринные окна и входная группа с колоннами и пандусом. Существующая колористика фасадов здания - светло-серого, зелёного, красного цветов.

2. Существующее состояние фасадов объекта (материал, колористика):
(подтверждается материалами фотофиксации) (в случае различных архитектурно-художественных характеристик фасадов описание производиться по каждому фасаду отдельно)

2.1. Кровля: рулонная;

2.2. Стены: металлокассеты серого цвета, металлокассеты зелёного цвета (входная группа); кирпич неокрашенный, светло-оранжевого цвета; мелкоразмерная керамическая плитка светло-жёлтого цвета;

2.3. Ограждение балконов и лоджий: нет;

2.4. Оконные блоки (переплет): ПВХ белого, зелёного цветов;

2.5. Дверные блоки: металл, окраска серого цвета; ПВХ зелёного цвета;

2.6. Цоколь: плитка серого цвета;

2.7. Лестницы: тротуарная плитка серого цвета;

2.8. Архитектурные детали: нет;

2.9. Иные поверхности: металлокассеты красного цвета (фриз).


https://moskvakadastr.ru/


3. Фотофиксация объекта

ВИД.1



ОБРАЗЦЫ ЦВЕТА (МЕТАЛЛОКАССЕТЫ).

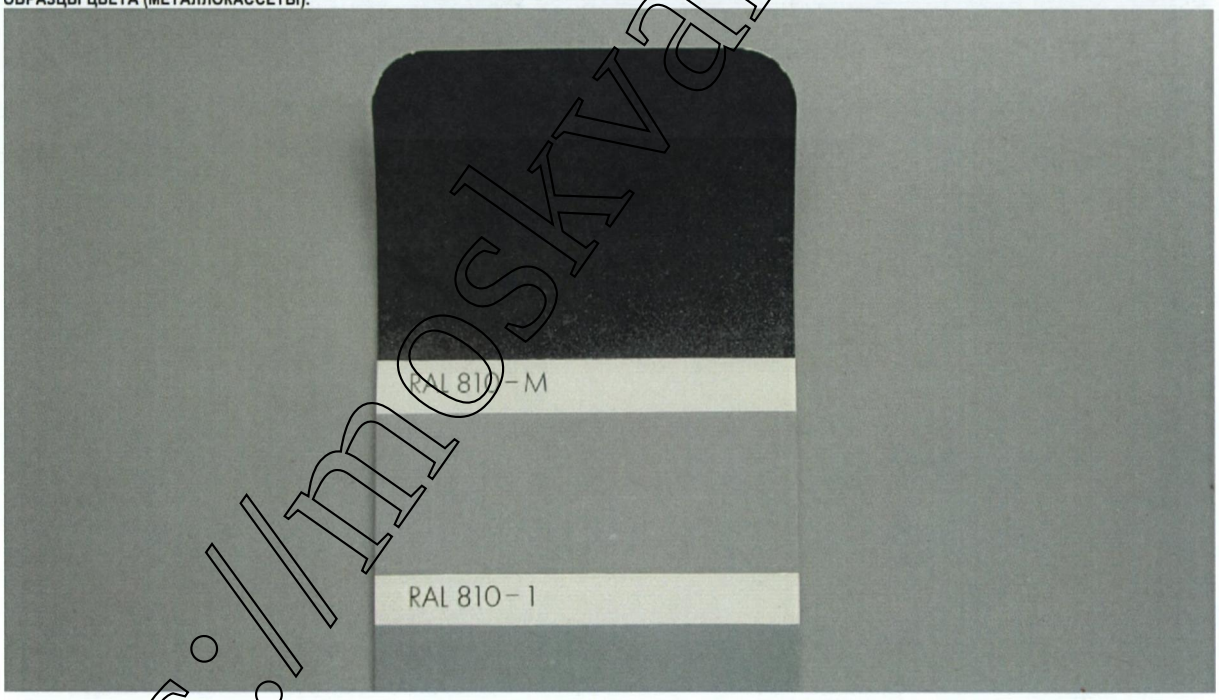

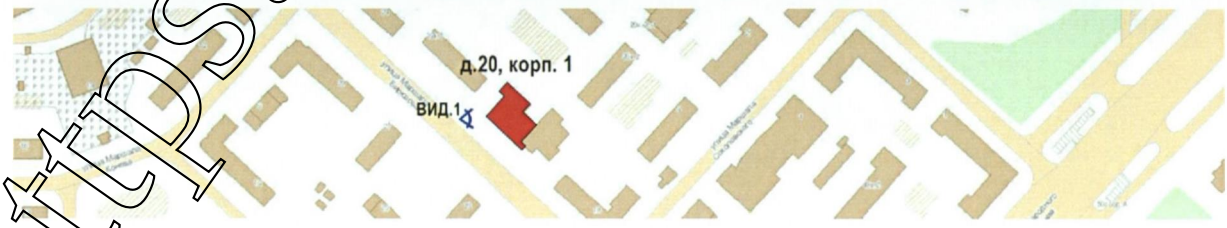

- рассматриваемое здание

Вид 1 - точки съемки

https://moskvakadastr.ru/


3. Фотофиксация объекта

ВИД.2



ОБРАЗЦЫ ЦВЕТА (ДВЕРИ).



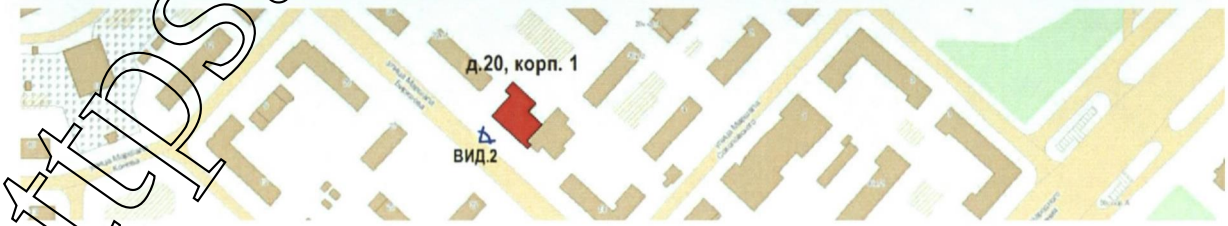

- рассматриваемое здание

Вид 1 - точки съемки

https://moskvakadastr.ru/


3. Фотофиксация объекта

ВИД.3



ВИД.4



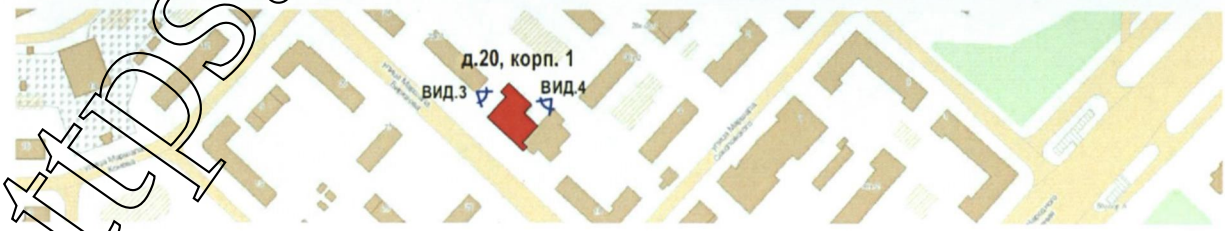

- рассматриваемое здание

Вид 1 - точки съемки

https://moskvakadastr.ru/


3. Фотофиксация объекта

ВИД.5



ВИД.6



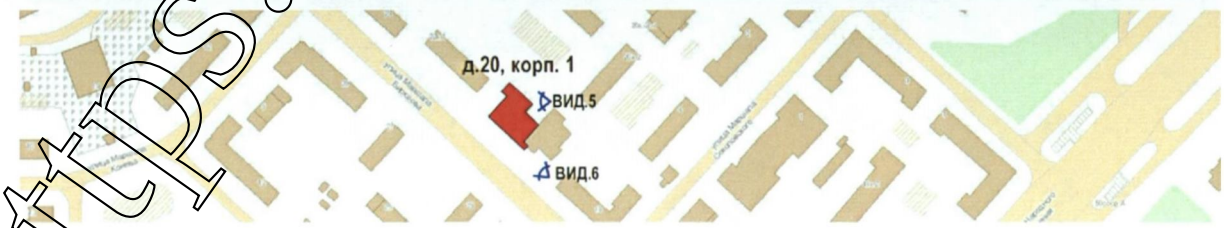



- рассматриваемое здание


Вид 1 - точки съемки

https://moskvakadastr.ru/

IV. ФАСАДЫ ОБЪЕКТА (М 1:100)

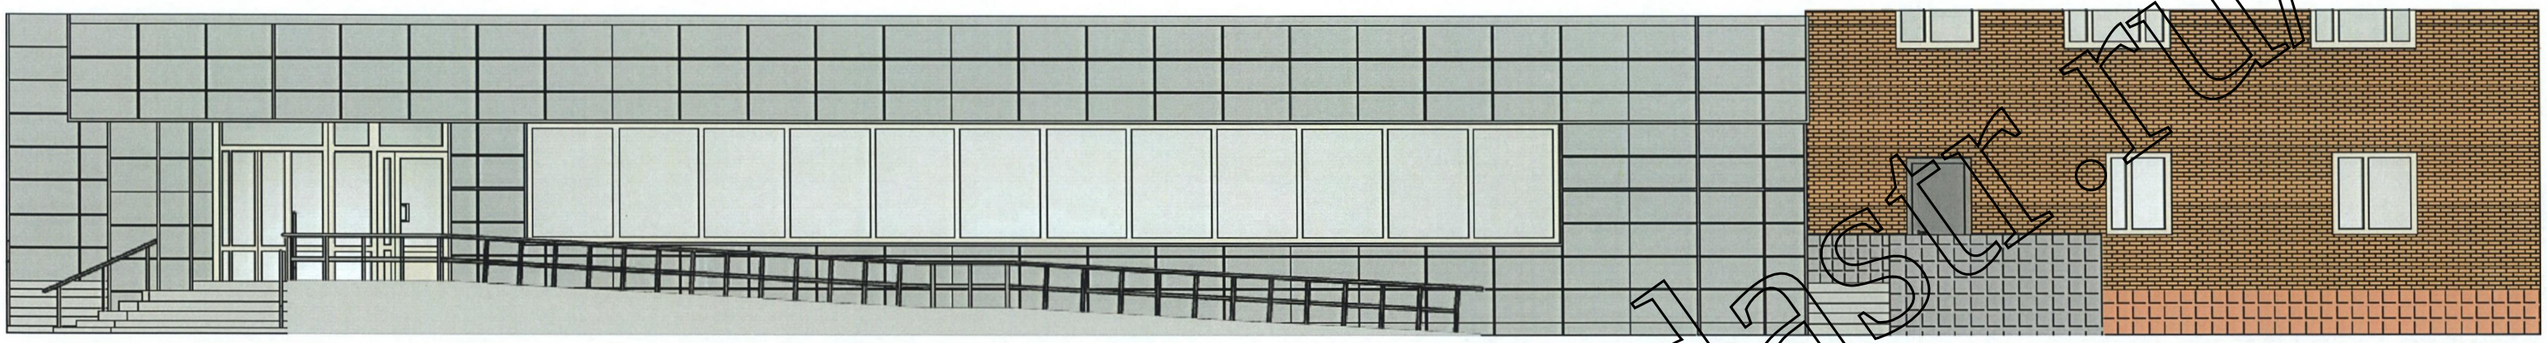

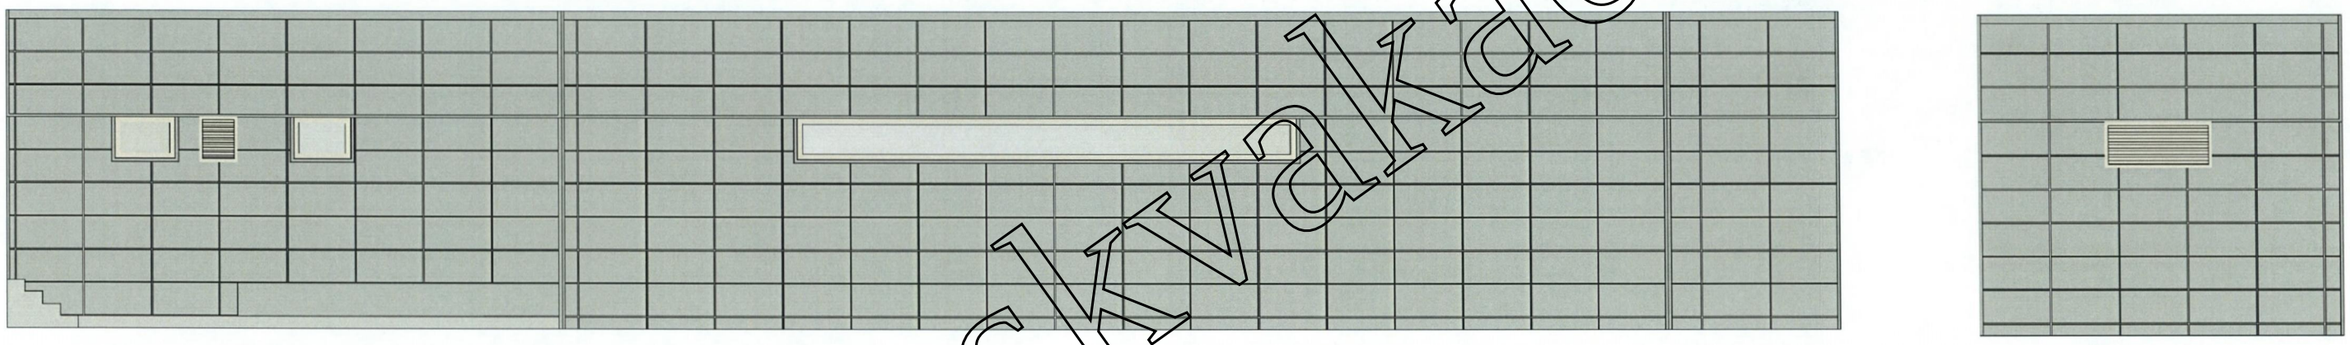

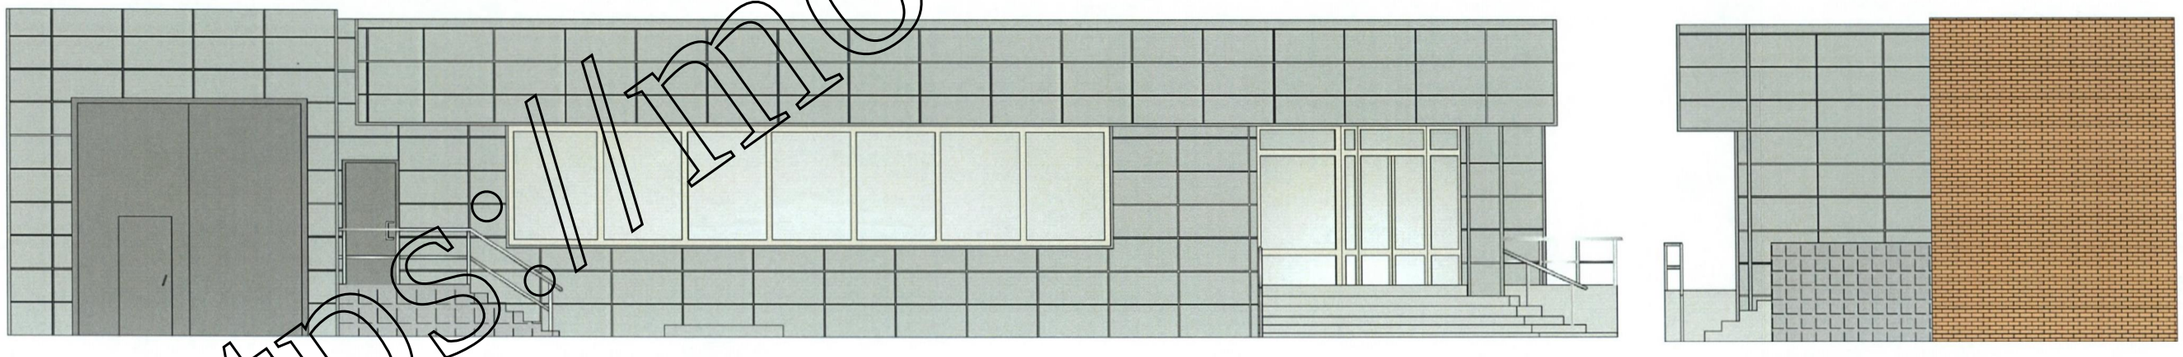

https://moskvakadastr.ru/

Адрес объекта : Маршала Бирюзова ул., д. 20, корп. 1.

Автор проектного решения : -.

№ п/п	Наименование элемента	Материал и/или вид отделки	Образец цвета	Марка цвета по политрам: NCS, RAL	Примечания
1	2	3	4	5	6
	Система водоотведения				
1	Кровля	рулонная			
2	Ограждение кровли				
3	Трубы водостока				
4	Подоконные отливы				
	Поверхности стен				
1	Стены	панель алюкобонд		NCS S 2500-N RAL 7035	вентилируемый фасад
		кирпич неокрашенный		NCS S 1030-Y30R RAL 1002	очистка
2	Карниз				
3	Пилястры				
4	Наличники				
5	Ограждение балконов				
6	Другие архитектурные элементы	панель алюкобонд		NCS S 2500-N RAL 7035	фриз, вентилируемый фасад
7	Цоколь	панель алюкобонд		NCS S 2500-N RAL 7035	вентилируемый фасад
		плитка		NCS S 2500-N RAL 7038	
		плитка		NCS S 1030-Y60R RAL 3012	

*Указан примерный перечень элементов фасадов.

*При окраске и отделке фасада согласовать колористическое решение с автором проекта

https://moskvakadastr.ru/

V. ОКРАСКА И ОТДЕЛКА В СООТВЕТСТВИИ С КОЛОРИСТИЧЕСКИМ РЕШЕНИЕМ ФАСАДОВ

№ п/п	Наименование элемента	Материал и/или вид отделки	Образец цвета	Марка цвета по политрам: NCS, RAL	Примечания
1	2	3	4	5	6
Заполнение проемов					
1	Оконный проём	металл, окраска (в заводских условиях)		NCS S 0300-N RAL 9010	
2	Дверной проём	металл, окраска (в заводских условиях)		NCS S 0300-N RAL 9010	
3	Слуховое окно				
4	Вентиляционный проём				
Входные группы					
1	Площадка входа	бетон		NCS S 2500-N RAL 7038	
2	Лестница	бетон		NCS S 2500-N RAL 7038	
3	Пандус	металл, окраска (в заводских условиях)		NCS S 2500-N RAL 7035	
4	Ограждение лестниц и пандуса	металл, окраска (в заводских условиях)		NCS S 2500-N RAL 7035	
5	Козырьки				
6	Ограждающая конструкция тамбура				
7	Фриз				
8	Прочее				

*Указан примерный перечень элементов фасадов.
* При окраске и отделке фасада согласовать колористическое решение с автором проекта

https://moskvakadastr.ru/