ДИЗАЙН-ПРОЕКТ РАЗМЕЩЕНИЯ ИНФОРМАЦИОННЫХ КОНСТРУКЦИЙ

*(данный **образец** может быть использован при подготовке **дизайн-проекта для размещения информационных конструкций**, на внешних поверхностях **торговых, развлекательных центров**, кинотеатров, театров, цирков)*

Адрес: *Указывается наименование улицы, номер дома*

Заказчик: *Указывается юридическое/физическое лицо, печать, подпись*

Исполнитель: *Указывается наименование организации/индивидуального предпринимателя*

ОБРАЗЕЦ

Москва 2021

ПОЯСНИТЕЛЬНАЯ ЗАПИСКА


Пояснительная записка включает:

- сведения об адресе объекта;
- сведения о типе и виде конструкции вывески;
- сведения о способе освещения вывески;
- параметры конструкции вывески (ширина, длина, высота);
- сведения о площади каждого фасада здания, строения, сооружения, на котором планируется размещение информационных конструкций (при размещении вывесок на внешних поверхностях торговых, развлекательных центров, кинотеатров, театров, цирков в границах территорий зон охраны объектов культурного наследия).
- при размещении уникальных информационных конструкций, исторический облик которых определен архитектурным проектом здания, к пояснительной записке прилагается информация (фото, архивные данные и иная информация), подтверждающая отношение вывески к информационным конструкциям, исторический облик которых определен архитектурным проектом здания.

ОБРАЗЕЦ

				Заказчик: Объект: Адрес:		
Должность	Фамилия	Подпись	Дата			
				Дизайн-проект размещения информационных конструкций	Стадия	Лист	Листов
					П	01	13
				Пояснительная записка	Исполнитель		

СХЕМА РАСПОЛОЖЕНИЯ ОБЪЕКТА

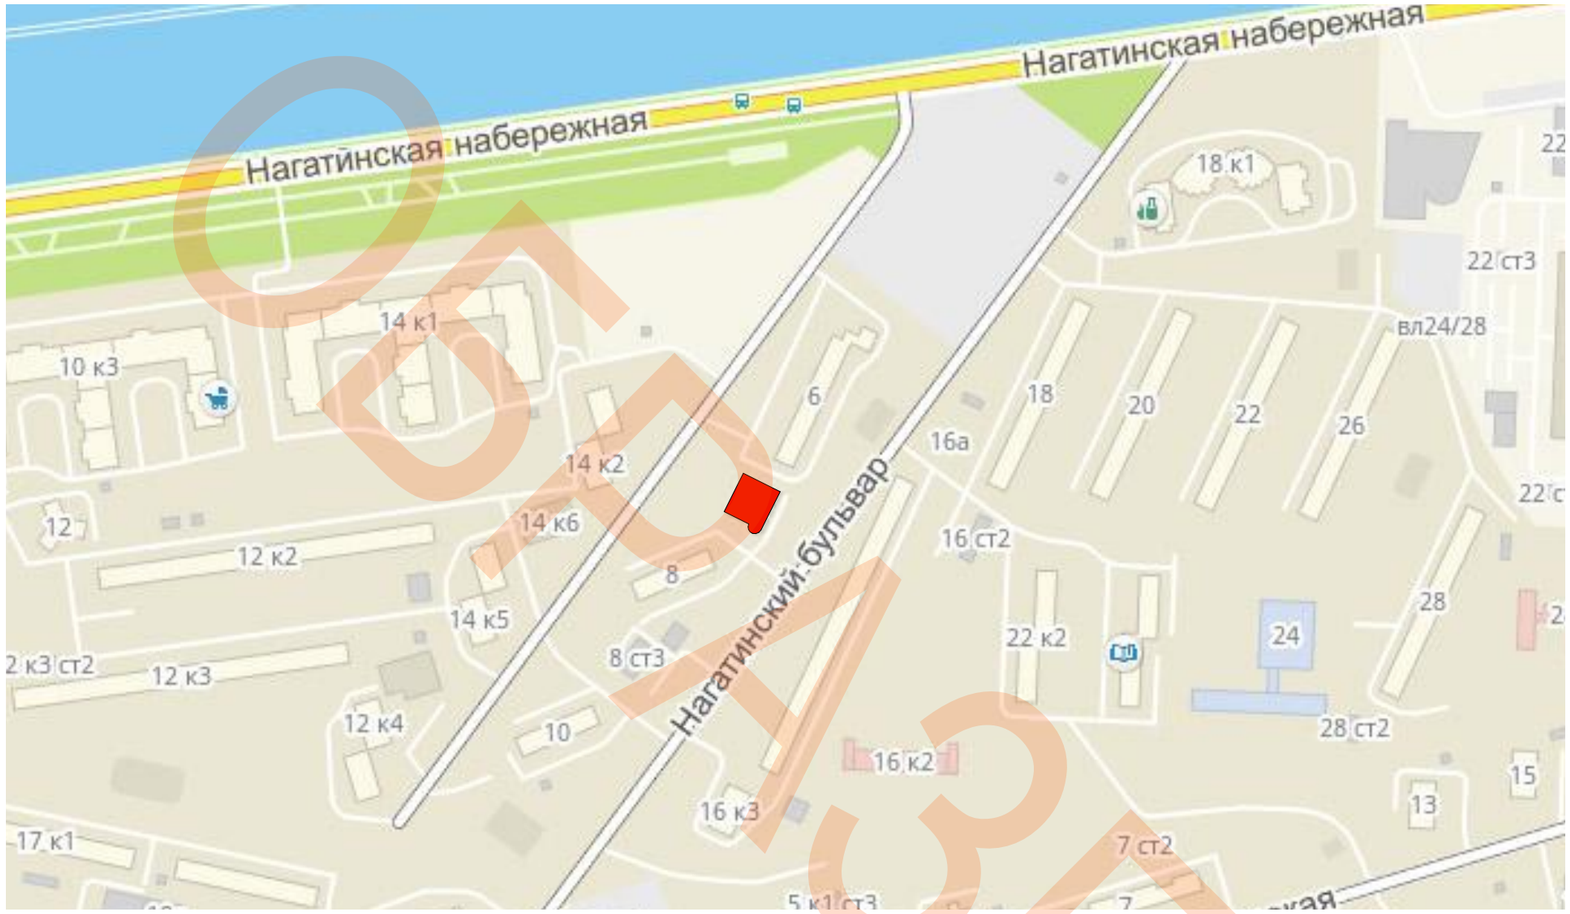

УСЛОВНЫЕ ОБОЗНАЧЕНИЯ

- рассматриваемый объект

				Заказчик: Объект: Адрес:			
Должность	Фамилия	Подпись	Дата				
				Дизайн-проект размещения информационных конструкций	Стадия	Лист	Листов
					П	02	13
				Схема расположения объекта	Исполнитель		

ОБРАЗЕЦ

Фотофиксация. Фасад 1



Фотофиксация. Фасад 2



Фотофиксация. Фасад 3



Фотофиксация. Фасад 4



* Фотографии должны быть выполнены
на момент подачи запроса о предоставлении государственной услуги,
всех внешних поверхностей объекта (фасады, крыши и иные поверхности).

				Заказчик: Объект: Адрес:			
Должность	Фамилия	Подпись	Дата				
				Дизайн-проект размещения информационных конструкций	Стадия	Лист	Листов
					П	03	13
				Фотофиксация. Вид 1	Исполнитель		

ЧЕРТЕЖ ФАСАДОВ И МЕСТА РАЗМЕЩЕНИЯ ИНФОРМАЦИОННЫХ КОНСТРУКЦИЙ С ПРИВЯЗКОЙ.
ФАСАД 1. М 1:100 *(без крышной информационной конструкции)*

Указывается масштаб разрабатываемого чертежа: М 1:50; М 1:100; М 1:200; М 1:500 (в зависимости от габаритных размеров объекта)

Схема типового крепления витринной информационной конструкции объемные буквы и знаки на подложке

Узел 1



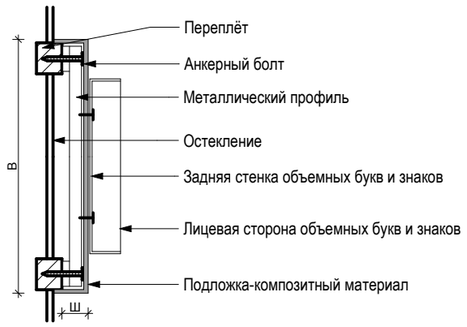


Схема типового крепления настенной информационной конструкции объемные буквы и знаки без подложки

Узел 2

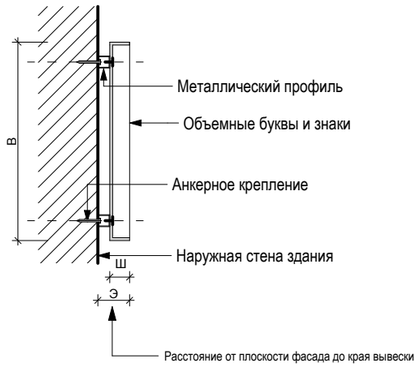


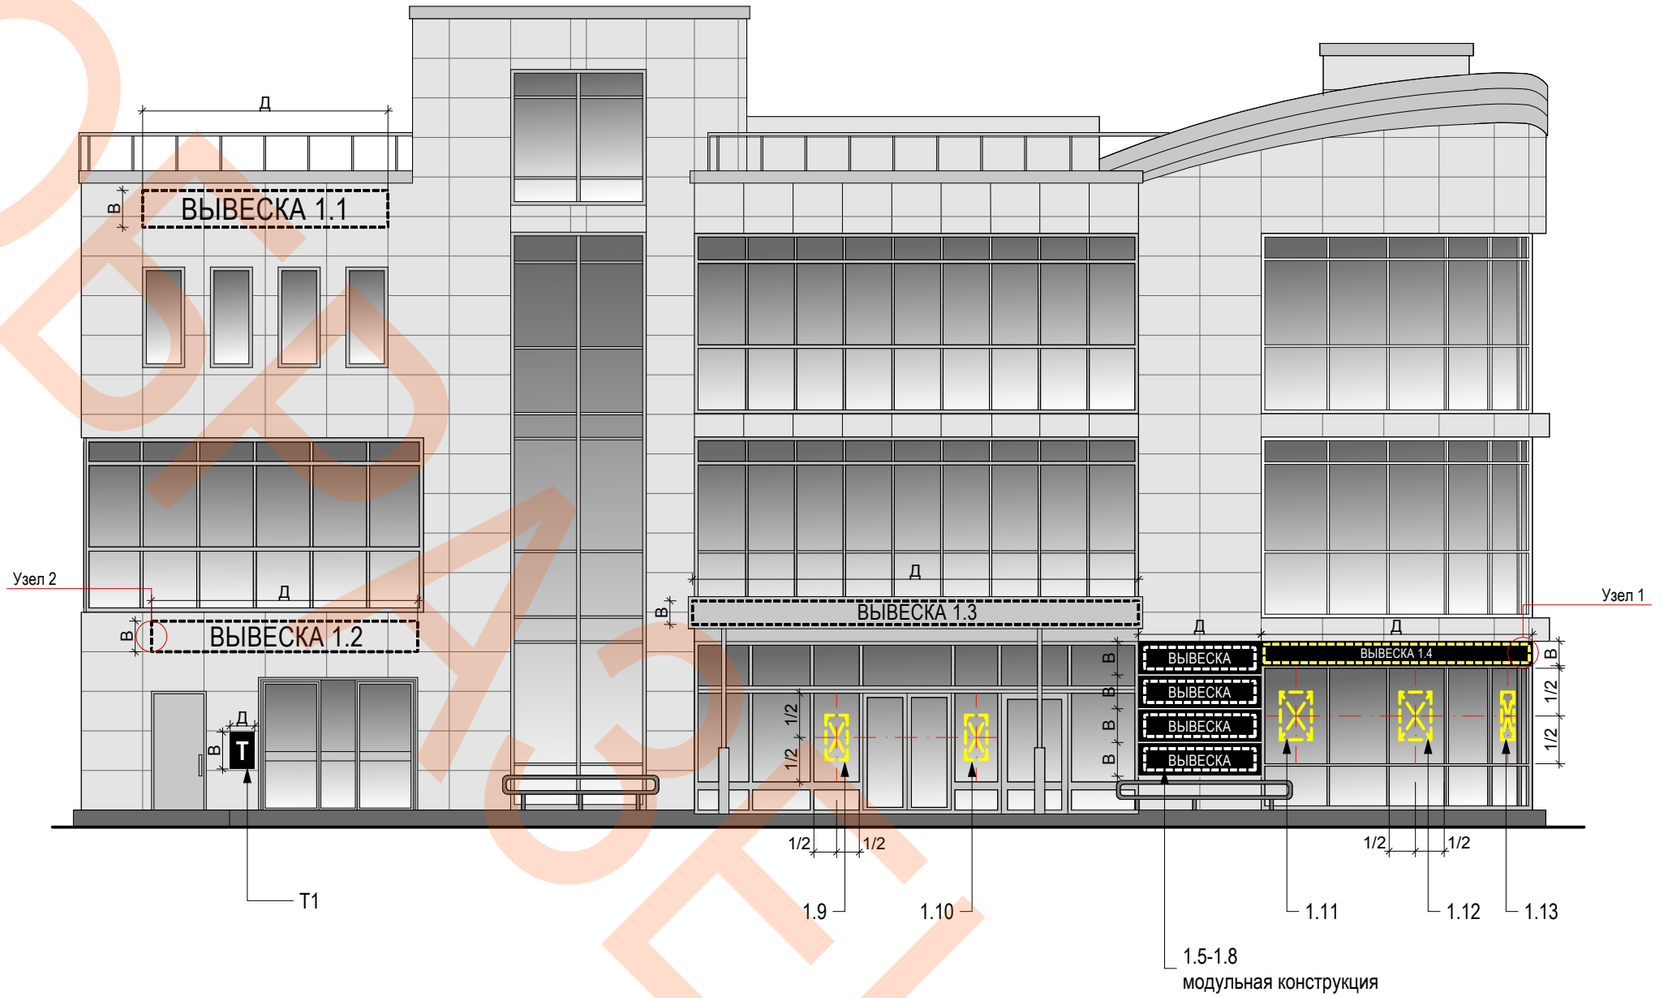

ЭКСПЛИКАЦИЯ ИНФОРМАЦИОННЫХ КОНСТРУКЦИЙ (ВЫВЕСОК)

№	Габаритные размеры (ДхВхШ) мм.	Тип конструкции	Вид конструкции Способ, тип освещения	Расстояние от плоскости фасада до края вывески. (мм.)
1.1	Д х В х Ш	Настенная	Объемные буквы и знаки с внутренним подсветом без подложки	Э
1.2	Д х В х Ш	Настенная	Объемные буквы и знаки с внутренним подсветом без подложки	Э
1.3	Д х В х Ш	Настенная	Объемные буквы и знаки с внутренним подсветом без подложки	Э
1.4	Д х В х Ш	Витринная	Объемные буквы и знаки с внутринним подсветом на подложке	———
1.5-1.8	Д х В х Ш	Настенная	Объемные буквы и знаки с внутренним подсветом на подложке модульная конструкция	Э
Т1	Д х В х Ш	Настенная	Информационная табличка	———
1.9-1.13	1/2 длины, 1/2 высоты витрины	Витринная (внутренняя)	Витринная конструкция (включая электронные носители и экраны)	———

Схема плана здания

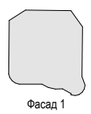

Фасад 1

Должность	Фамилия	Подпись	Дата	
				Заказчик: Объект: Адрес:
				Дизайн-проект размещения информационных конструкций
				Чертеж фасадов и места размещения информационных конструкций с привязкой

Стадия	Лист	Листов
П	04	13

Исполнитель

Образец

ЧЕРТЕЖ ФАСАДОВ И МЕСТА РАЗМЕЩЕНИЯ ИНФОРМАЦИОННЫХ КОНСТРУКЦИЙ С ПРИВЯЗКОЙ.
ФАСАД 2. М 1:100

Указывается масштаб разрабатываемого чертежа: М 1:50; М 1:100; М 1:200; М 1:500
(в зависимости от габаритных размеров объекта)

Схема типового крепления витринной информационной конструкции
объемные буквы и знаки на подложке

Узел 1



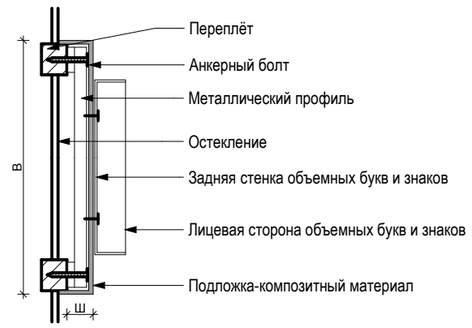


Схема типового крепления настенной информационной конструкции
объемные буквы и знаки без подложки

Узел 2

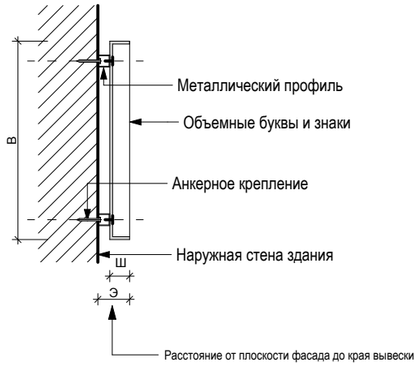

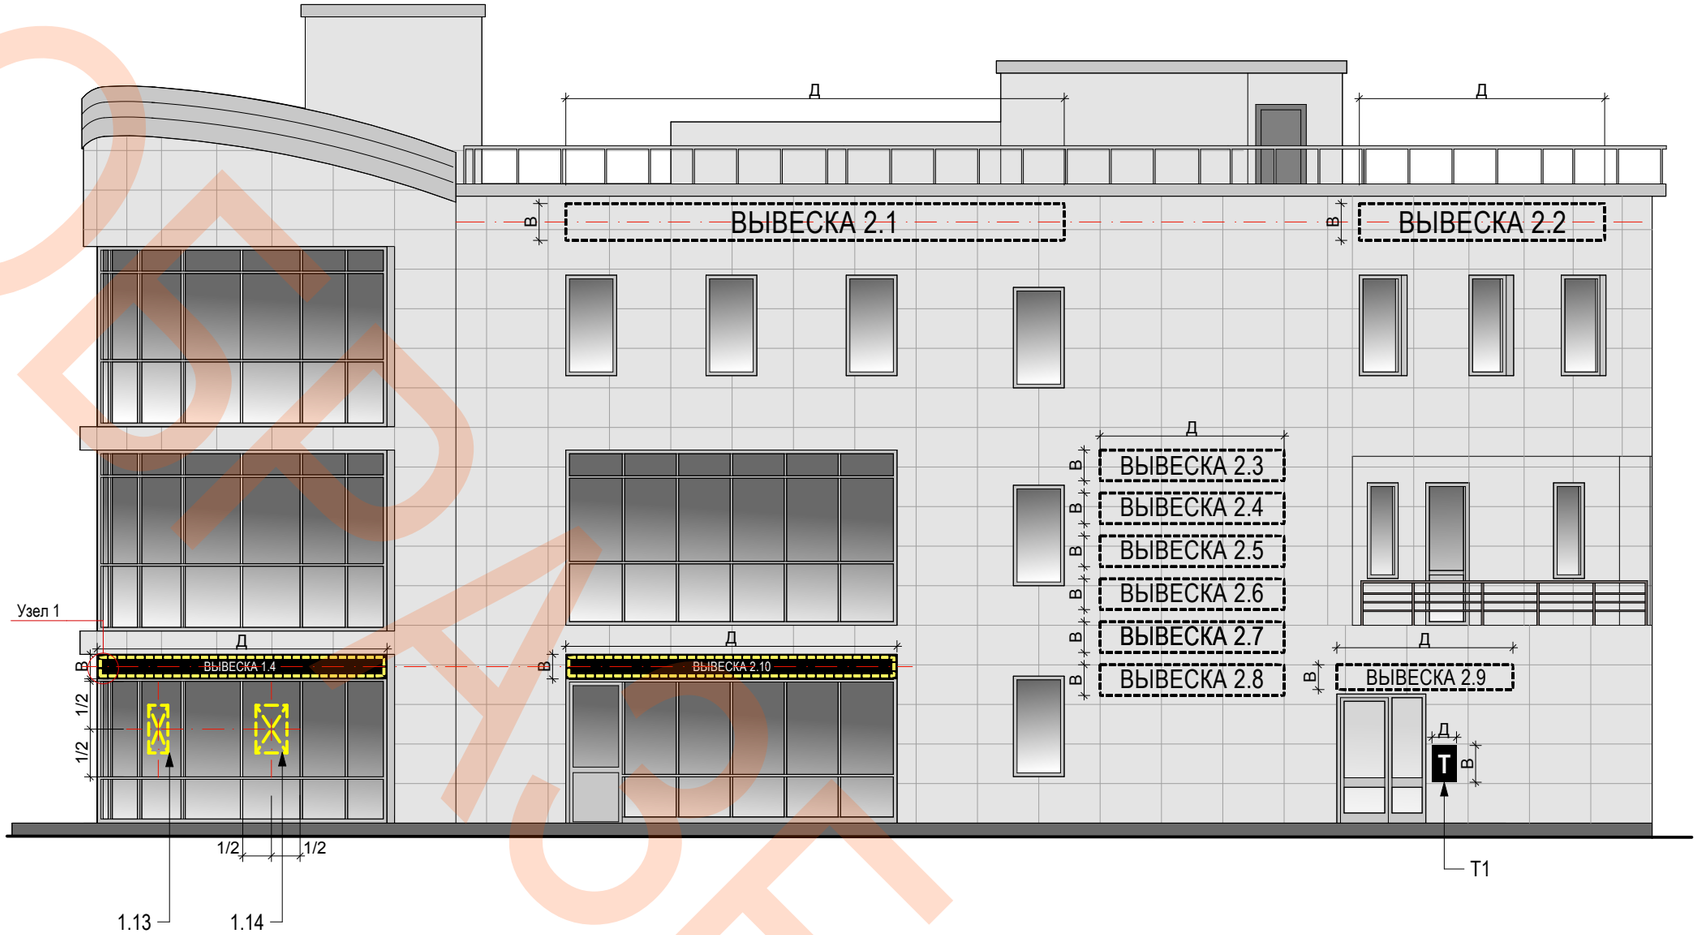

ЭКСПЛИКАЦИЯ ИНФОРМАЦИОННЫХ КОНСТРУКЦИЙ (ВЫВЕСОК)

№	Габаритные размеры (ВхДхШ) мм.	Тип конструкции	Вид конструкции Способ, тип освещения	Расстояние от плоскости фасада до края вывески. (мм.)
2.1	Д х В х Ш	Настенная	Объемные буквы и знаки с внутренним подсветом без подложки	Э
2.2	Д х В х Ш	Настенная	Объемные буквы и знаки с внутренним подсветом без подложки	Э
1.4	Д х В х Ш	Витринная	Объемные буквы и знаки с внутренним посветом на подложке	———
2.10	Д х В х Ш	Витринная	Объемные буквы и знаки с внутренним посветом на подложке	———
2.3-2.8	Д х В х Ш	Настенная	Объемные буквы и знаки с внутренним подсветом без подложки	Э
2.9	Д х В х Ш	Настенная	Объемные буквы и знаки с внутренним подсветом без подложки	Э
Т1	Д х В х Ш	Настенная	Информационная табличка	———
1.13-1.14	1/2 длины, 1/2 высоты витрины	Витринная	Витринная конструкция (включая электронные носители и экраны)	———

Схема плана здания



				Заказчик: Объект: Адрес:			
Должность	Фамилия	Подпись	Дата				
				Дизайн-проект размещения информационных конструкций	Стадия	Лист	Листов
					П	05	13
				Четреж фасадов и места размещения информационных конструкций с привязкой	Исполнитель		

ОБРАЗЕЦ

ФОТОМОНТАЖ*. ВИД 1
(без крышной информационной конструкции)


ФАСАД 1



ЭКСПЛИКАЦИЯ ИНФОРМАЦИОННЫХ КОНСТРУКЦИЙ (ВЫВЕСОК)

№	Габаритные размеры (ДхВхШ) мм.	Тип конструкции	Вид конструкции Способ, тип освещения	Расстояние от плоскости фасада до края вывески. (мм.)
1.1	Д х В х Ш	Настенная	Объемные буквы и знаки с внутренним подсветом без подложки	Э
1.2	Д х В х Ш	Настенная	Объемные буквы и знаки с внутренним подсветом без подложки	Э
1.3	Д х В х Ш	Настенная	Объемные буквы и знаки с внутренним подсветом без подложки	Э
1.4	Д х В х Ш	Витринная	Объемные буквы и знаки с внутринним подсветом на подложке	———
1.5-1.8	Д х В х Ш	Настенная	Объемные буквы и знаки с внутренним подсветом на подложке модульная конструкция	Э
Т1	Д х В х Ш	Настенная	Информационная табличка	———
1.9-1.13	1/2 длины, 1/2 высоты витрины	Витринная (внутренняя)	Витринная конструкция (включая электронные носители и экраны)	———

Схема плана здания

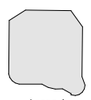

* Фотомонтаж должен обеспечить в полном объеме четкую демонстрацию предполагаемого места размещения вывески и всех иных конструкций, размещенных на всех внешних поверхностей здания,а также не содержать иных объектов припятствующих указанной демонстрации, в том числе автомобильный транспорт.
Фотографии должны быть выполнены на момент подачи запроса о предоставлении государственной услуги.


Должность	Фамилия	Подпись	Дата

Заказчик:
Объект:
Адрес:

Дизайн-проект размещения информационных конструкций	Стадия	Лист	Листов
	П	06	13
Фотомонтаж. Вид 1	Исполнитель		

ФОТОМОНТАЖ*. ВИД 2
(без крышной информационной конструкции)

ФАСАД 2

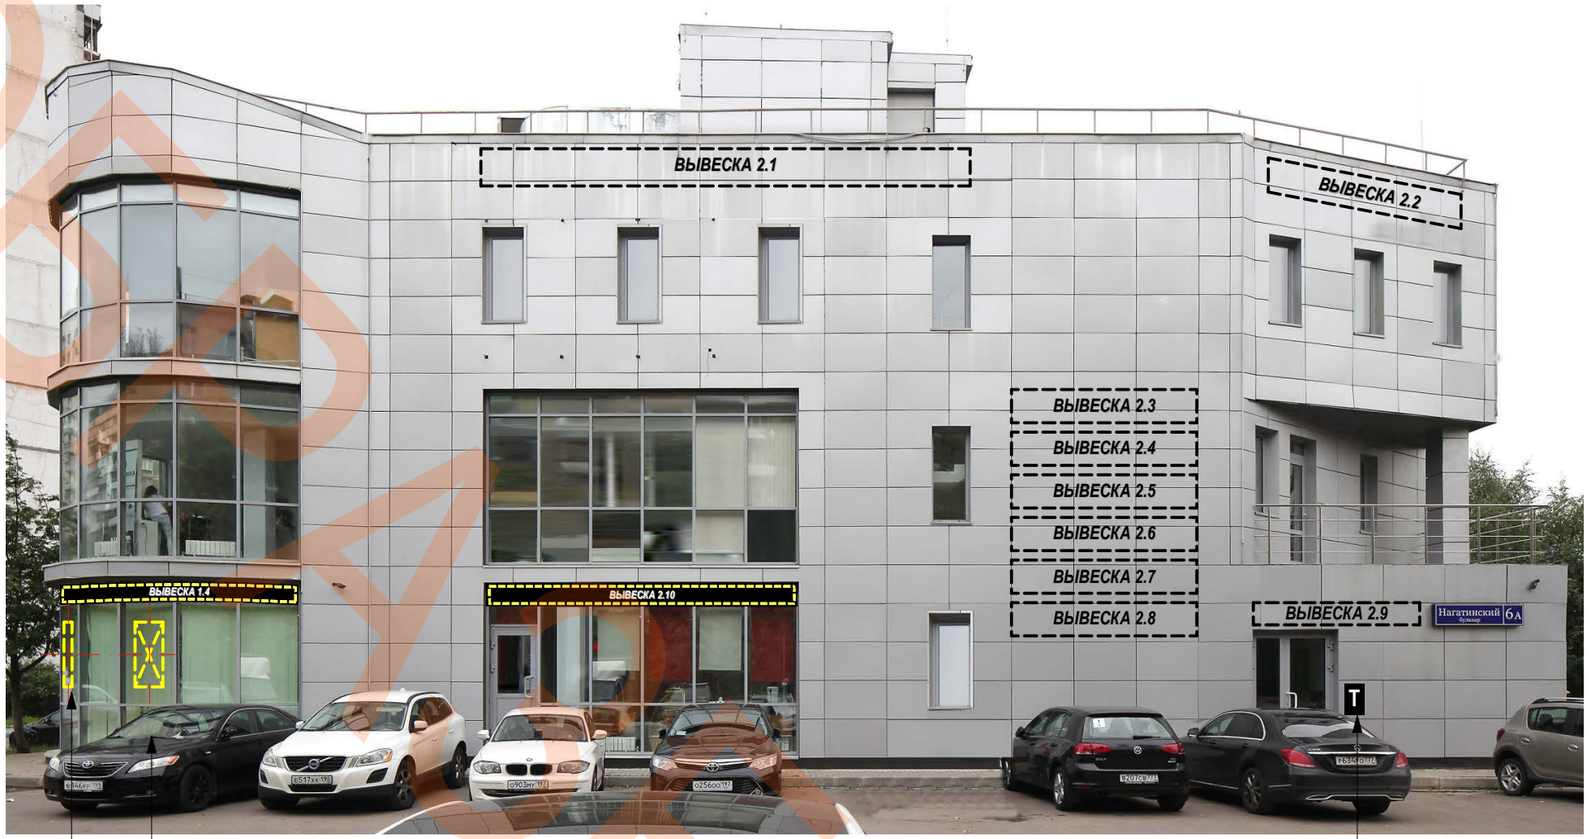

ЭКСПЛИКАЦИЯ ИНФОРМАЦИОННЫХ КОНСТРУКЦИЙ (ВЫВЕСОК)

№	Габаритные размеры (ВхДхШ) мм.	Тип конструкции	Вид конструкции Способ, тип освещения	Расстояние от плоскости фасада до края вывески. (мм.)
2.1	Д х В х Ш	Настенная	Объемные буквы и знаки с внутренним подсветом без подложки	Э
2.2	Д х В х Ш	Настенная	Объемные буквы и знаки с внутренним подсветом без подложки	Э
1.4	Д х В х Ш	Витринная	Объемные буквы и знаки с внитренним посветом на подложке	———
2.10	Д х В х Ш	Витринная	Объемные буквы и знаки с внитренним посветом на подложке	———
2.3-2.8	Д х В х Ш	Настенная	Объемные буквы и знаки с внутренним подсветом без подложки	Э
2.9	Д х В х Ш	Настенная	Объемные буквы и знаки с внутренним подсветом без подложки	Э
Т1	Д х В х Ш	Настенная	Информационная табличка	———
1.13-1.14	1/2 длины, 1/2 высоты витрины	Витринная	Витринная конструкция (включая электронные носители и экраны)	———

Схема плана здания



* Фотомонтаж должен обеспечить в полном объеме четкую демонстрацию предполагаемого места размещения вывески и всех иных конструкций, размещенных на всех внешних поверхностей здания,а также не содержать иных объектов припятствующих указанной демонстрации, в том числе автомобильный транспорт.
Фотографии должны быть выполнены на момент подачи запроса о предоставлении государственной услуги.

Должность	Фамилия	Подпись	Дата	Заказчик: Объект: Адрес:			
				Дизайн-проект размещения информационных конструкций	Стадия	Лист	Листов
					П	07	13
				Фотомонтаж. Вид 2	Исполнитель		

ОБРАЗЕЦ

ДЛЯ КРЫШНЫХ ИНФОРМАЦИОННЫХ КОНСТРУКЦИЙ*


ЧЕРТЕЖ ФАСАДОВ И МЕСТА РАЗМЕЩЕНИЯ ИНФОРМАЦИОННЫХ КОНСТРУКЦИЙ С ПРИВЯЗКОЙ.

ФАСАД 1. М 1:100


Указывается масштаб разрабатываемого чертежа: М 1:50; М 1:100; М 1:200; М 1:500 (в зависимости от габаритных размеров объекта)

СХЕМА ТИПОВОГО КРЕПЛЕНИЯ КРЫШНОЙ ИНФОРМАЦИОННОЙ КОНСТРУКЦИИ


ВИД СБОКУ

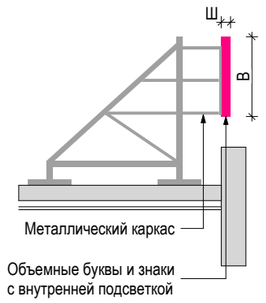


ВИД СВЕРХУ

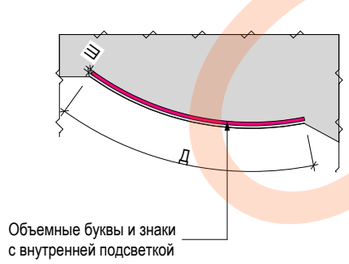

ВИД ОСНОВНОЙ

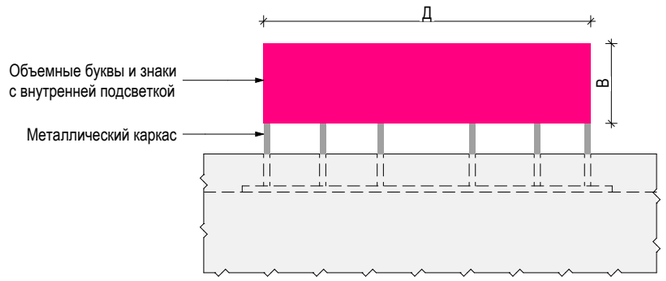

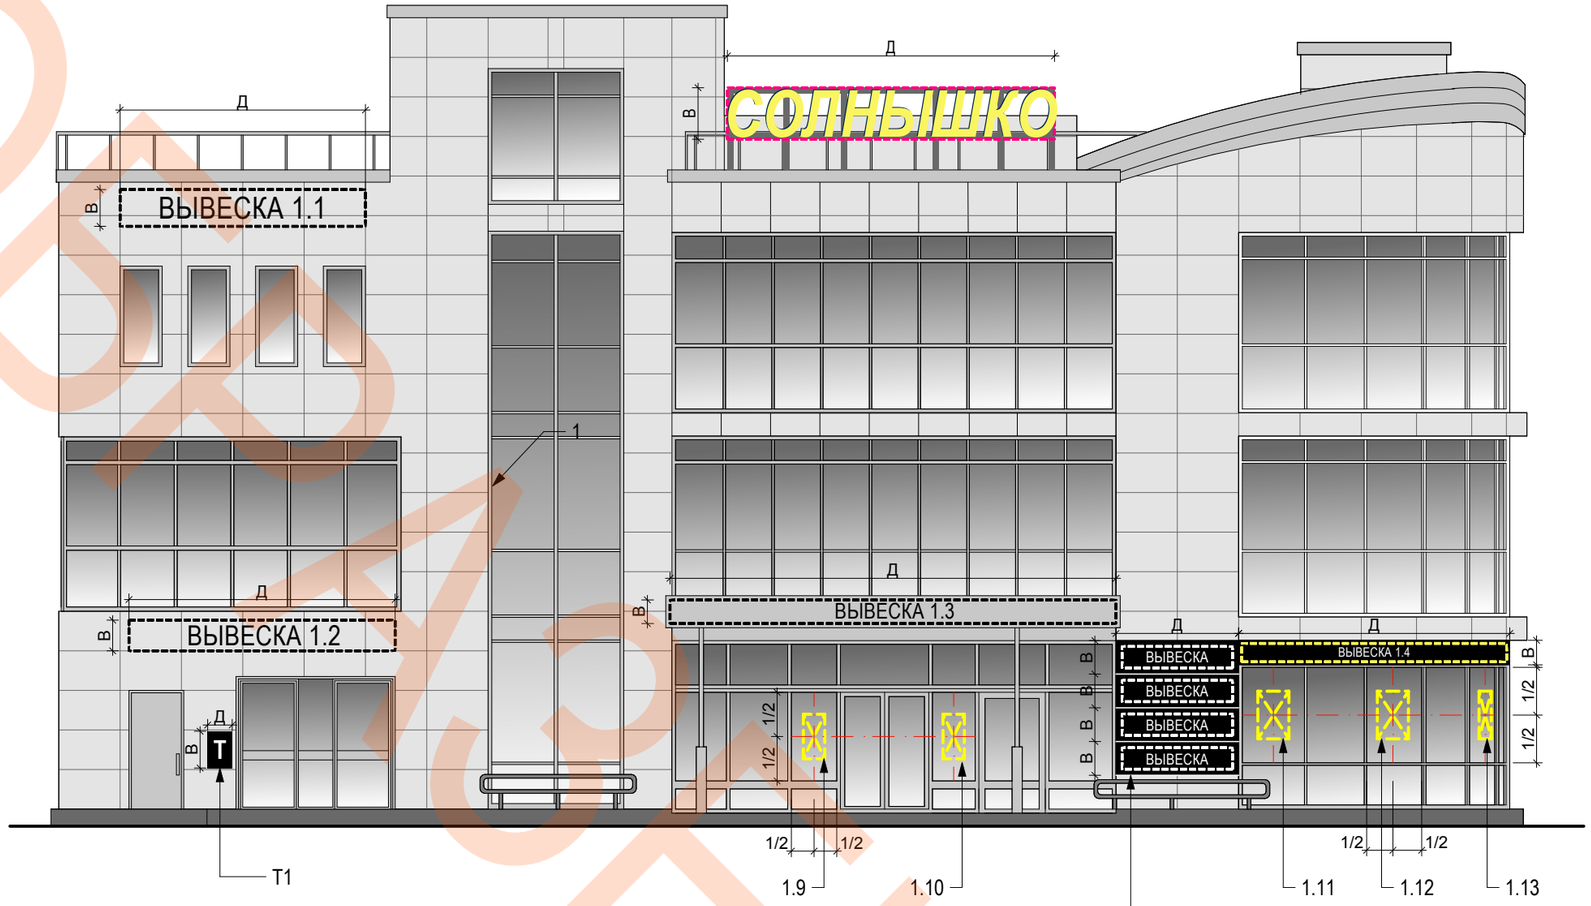


ЭКСПЛИКАЦИЯ ИНФОРМАЦИОННЫХ КОНСТРУКЦИЙ (ВЫВЕСОК)

№	Габаритные размеры (ДхВхШ) мм.	Тип конструкции	Вид конструкции Способ, тип освещения
1	Д х В х Ш	Крышная	Объемные буквы и знаки с Внутренней подсветкой

ЭКСПЛИКАЦИЯ ИНФОРМАЦИОННЫХ КОНСТРУКЦИЙ (ВЫВЕСОК)

№	Габаритные размеры (ДхВхШ) мм.	Тип конструкции	Вид конструкции Способ, тип освещения	Расстояние от плоскости фасада до края вывески. (мм.)
1.1	Д х В х Ш	Настенная	Объемные буквы и знаки с внутренним подсветом без подложки	Э
1.2	Д х В х Ш	Настенная	Объемные буквы и знаки с внутренним подсветом без подложки	Э
1.3	Д х В х Ш	Настенная	Объемные буквы и знаки с внутренним подсветом без подложки	Э
1.4	Д х В х Ш	Витринная	Объемные буквы и знаки с внутринним подсветом на подложке	———
1.5-1.8	Д х В х Ш	Настенная	Объемные буквы и знаки с внутренним подсветом на подложке модульная конструкция	Э
Т1	Д х В х Ш	Настенная	Информационная табличка	———
1.9-1.13	1/2 длины, 1/2 высоты витрины	Витринная (внутренняя)	Витринная конструкция (включая электронные носители и экраны)	———

Схема плана здания

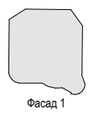

Должность	Фамилия	Подпись	Дата

Заказчик:
Объект:
Адрес:

Дизайн-проект размещения информационных конструкций	Стадия	Лист	Листов
	П	08	13
Схема размещения информационной конструкциис привязкой.Фасад 1.	Исполнитель		

ОБРАЗЕЦ

ФОТОМОНТАЖ*. ВИД 1

ЭКСПЛИКАЦИЯ ИНФОРМАЦИОННЫХ КОНСТРУКЦИЙ (ВЫВЕСОК)

№	Габаритные размеры (ДхВхШ) мм.	Тип конструкции	Вид конструкции Способ, тип освещения
1	Д х В х Ш	Крышная	Объемные буквы и знаки с Внутренней подсветкой

ЭКСПЛИКАЦИЯ ИНФОРМАЦИОННЫХ КОНСТРУКЦИЙ (ВЫВЕСОК)

№	Габаритные размеры (ДхВхШ) мм.	Тип конструкции	Вид конструкции Способ, тип освещения	Расстояние от плоскости фасада до края вывески. (мм.)
1.1	Д х В х Ш	Настенная	Объемные буквы и знаки с внутренним подсветом без подложки	Э
1.2	Д х В х Ш	Настенная	Объемные буквы и знаки с внутренним подсветом без подложки	Э
1.3	Д х В х Ш	Настенная	Объемные буквы и знаки с внутренним подсветом без подложки	Э
1.4	Д х В х Ш	Витринная	Объемные буквы и знаки с внутринним подсветом на подложке	———
1.5-1.8	Д х В х Ш	Настенная	Объемные буквы и знаки с внутренним подсветом на подложке модульная конструкция	Э
Т1	Д х В х Ш	Настенная	Информационная табличка	———
1.9-1.13	1/2 длины, 1/2 высоты витрины	Витринная (внутренняя)	Витринная конструкция (включая электронные носители и экраны)	———

ФАСАД 1



Схема плана здания



Фасад 1

* Фотомонтаж должен обеспечить в полном объеме четкую демонстрацию предполагаемого места размещения вывески и всех иных конструкций, размещенных на всех внешних поверхностей здания,а также не содержать иных объектов припятствующих указанной демонстрации, в том числе автомобильный транспорт.
Фотографии должны быть выполнены на момент подачи запроса о предоставлении государственной услуги.

				Заказчик: Объект: Адрес:			
Должность	Фамилия	Подпись	Дата				
				Дизайн-проект размещения информационных конструкций	Стадия	Лист	Листов
					П	09	13
				Фотомонтаж. Вид 1	Исполнитель		