ДИЗАЙН-ПРОЕКТ РАЗМЕЩЕНИЯ ИНФОРМАЦИОННЫХ КОНСТРУКЦИЙ

(данный образец может быть использован при подготовке дизайн-проекта в случае необходимости внесения изменений в утвержденную Архитектурно-художественную концепцию)

ОБРАЗЕЦ

Адрес: *Указывается наименование улицы, номер дома*

Заказчик: *Указывается юридическое/физическое лицо, печать, подпись*

Исполнитель: *Указывается наименование организации/индивидуального предпринимателя*

Москва 2021

ПОЯСНИТЕЛЬНАЯ ЗАПИСКА


Пояснительная записка включает:

- сведения об адресе объекта;
- сведения о типе и виде конструкции вывески;
- сведения о способе освещения вывески;
- параметры конструкции вывески (ширина, длина, высота);
- сведения о площади каждого фасада здания, строения, сооружения, на котором планируется размещение информационных конструкций (при размещении вывесок на внешних поверхностях торговых, развлекательных центров, кинотеатров, театров, цирков в границах территорий зон охраны объектов культурного наследия).
- при размещении уникальных информационных конструкций, исторический облик которых определен архитектурным проектом здания, к пояснительной записке прилагается информация (фото, архивные данные и иная информация), подтверждающая отношение вывески к информационным конструкциям, исторический облик которых определен архитектурным проектом здания.

ОБРАЗЕЦ

				Заказчик: Объект: Адрес:		
Должность	Фамилия	Подпись	Дата			
Архитектор				Дизайн-проект размещения информационных конструкций	Стадия	Лист	Листов
					П	01	08
				Пояснительная записка	Исполнитель		

СХЕМА РАСПОЛОЖЕНИЯ ОБЪЕКТА

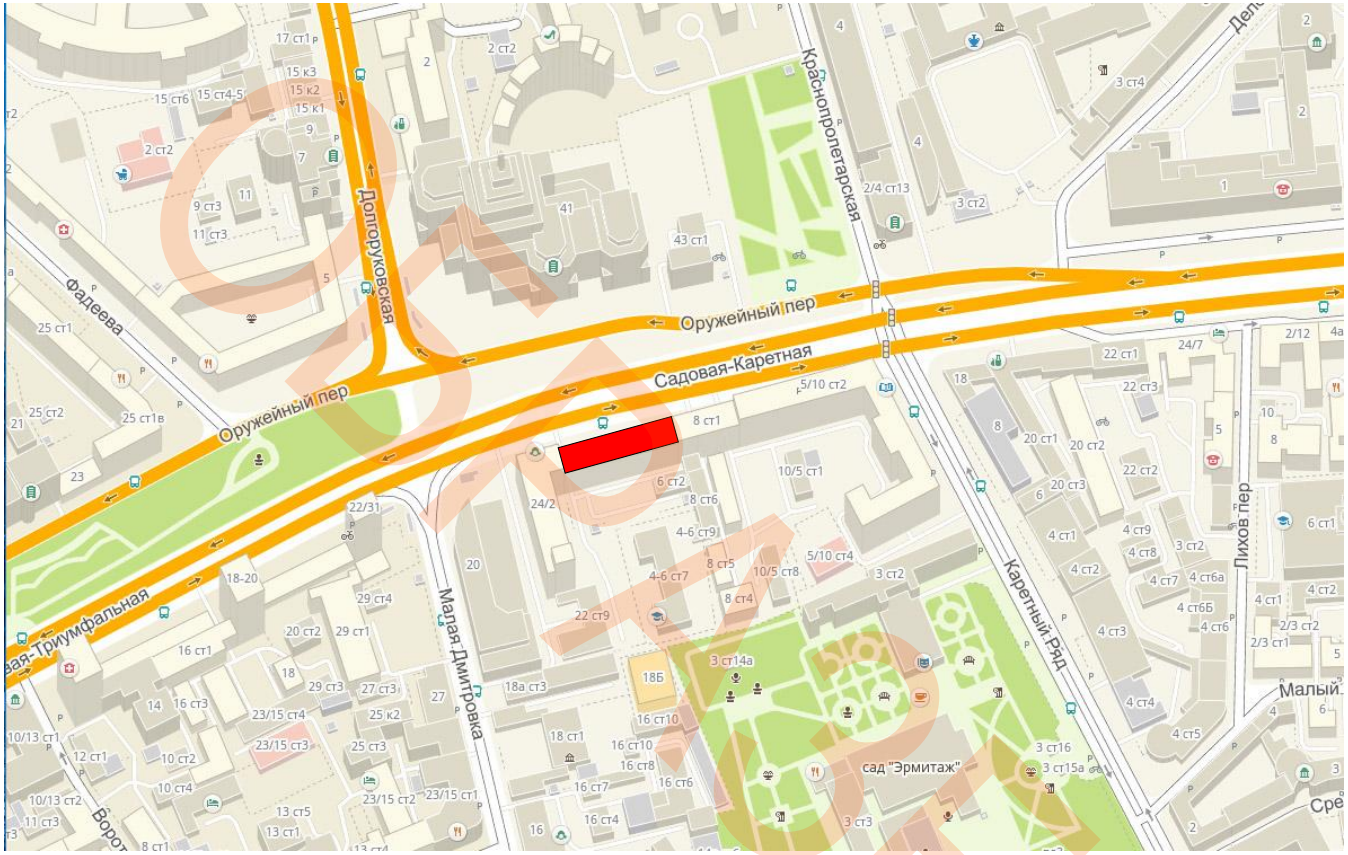

УСЛОВНЫЕ ОБОЗНАЧЕНИЯ

- рассматриваемый объект

				Заказчик:			
				Объект:			
				Адрес:			
Должность	Фамилия	Подпись	Дата				
Архитектор				Дизайн-проект размещения информационных конструкций	Стадия	Лист	Листов
					П	02	08
				Схема расположения объекта	Исполнитель		

ФРАГМЕНТ АРХИТЕКТУРНО-ХУДОЖЕСТВЕННОЙ КОНЦЕПЦИИ* ПО УЛ. САДОВАЯ-КАРЕТНАЯ

Садовая-Каретная ул., д. 4-6, стр. 1 (лист 2 из 2)

Анализ существующего положения



2

Схема размещения



Настенные информационные конструкции

- «Зеленая зона» размещения вывесок
- Вывеска — Объемные отдельностоящие буквы и знаки без подложки
- Вывеска — Объемные отдельностоящие буквы и знаки на плоской подложке

- T — Табличка
- M — Меню

Консольная информационная конструкция

- Панель-кронштейн

Витринные информационные конструкции

- Вывеска — Объемные отдельностоящие буквы и знаки без подложки
- Внутренняя информационная конструкция
- Вывеска — Объемные отдельностоящие буквы и знаки на плоской подложке

Соответствие правилам

- Соответствует правилам
- Не соответствует правилам

Схема плана

1 2

ГУП «ГлавАПУ»

125


КОМИТЕТ ПО АРХИТЕКТУРЕ И ГРАДОСТРОИТЕЛЬСТВУ ГОРОДА МОСКВЫ

ОБРАЗЕЦ

				Заказчик: Объект: Адрес:		
Должность	Фамилия	Подпись	Дата			
Архитектор				Дизайн-проект размещения информационных конструкций	Стадия: П Лист: 03 Листов: 08	
				Фрагмент архитектурно-художественной концепции по ул. Новый Арбат	Исполнитель	

* Архитектурно-Художественные концепции размещены на официальном сайте Москомархитектуры. эл.адрес www.mos.ru/mka

ФОТОФИКСАЦИЯ*. ВИД 1

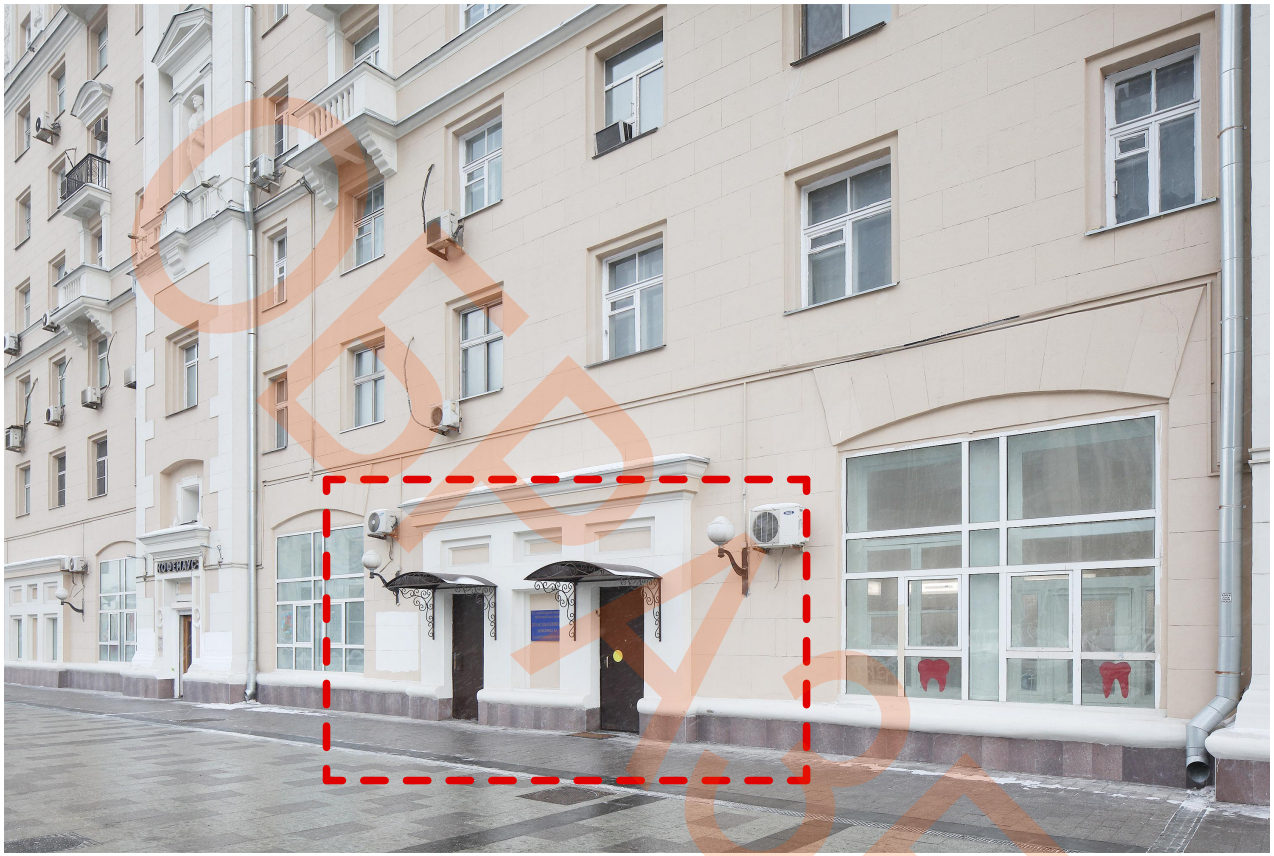


ОБРАЗЕЦ

				Заказчик:			
				Объект:			
				Адрес:			
Должность	Фамилия	Подпись	Дата				
Архитектор				Дизайн-проект размещения информационных конструкций	Стадия	Лист	Листов
					П	04	08
				Фотофиксация. Вид 1	Исполнитель		

* Фотографии должны быть выполнены
на момент подачи запроса о предоставлении государственной услуги,
всех внешних поверхностей объекта (фасады, крыши и иные поверхности).

ФОТОФИКСАЦИЯ*. ВИД 2

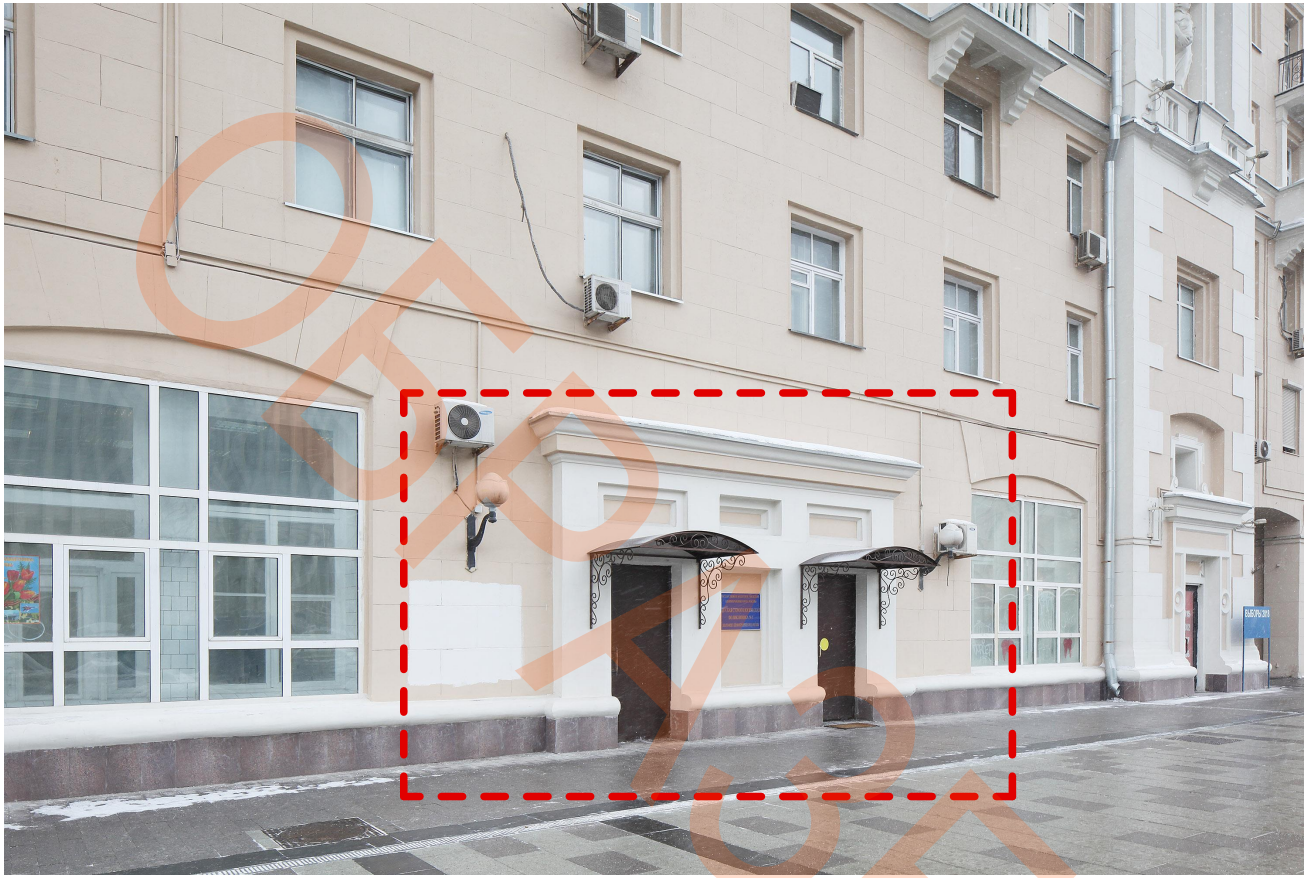


ОБРАЗЕЦ

				Заказчик:			
				Объект:			
Должность	Фамилия	Подпись	Дата	Адрес:			
Архитектор				Дизайн-проект размещения информационных конструкций	Стадия	Лист	Листов
					П	05	08
				Фотофиксация. Вид 2	Исполнитель		

* Фотографии должны быть выполнены
на момент подачи запроса о предоставлении государственной услуги,
всех внешних поверхностей объекта (фасады, крыши и иные поверхности).

ЧЕРТЕЖ ФАСАДОВ И МЕСТА РАЗМЕЩЕНИЯ ИНФОРМАЦИОННЫХ КОНСТРУКЦИЙ*

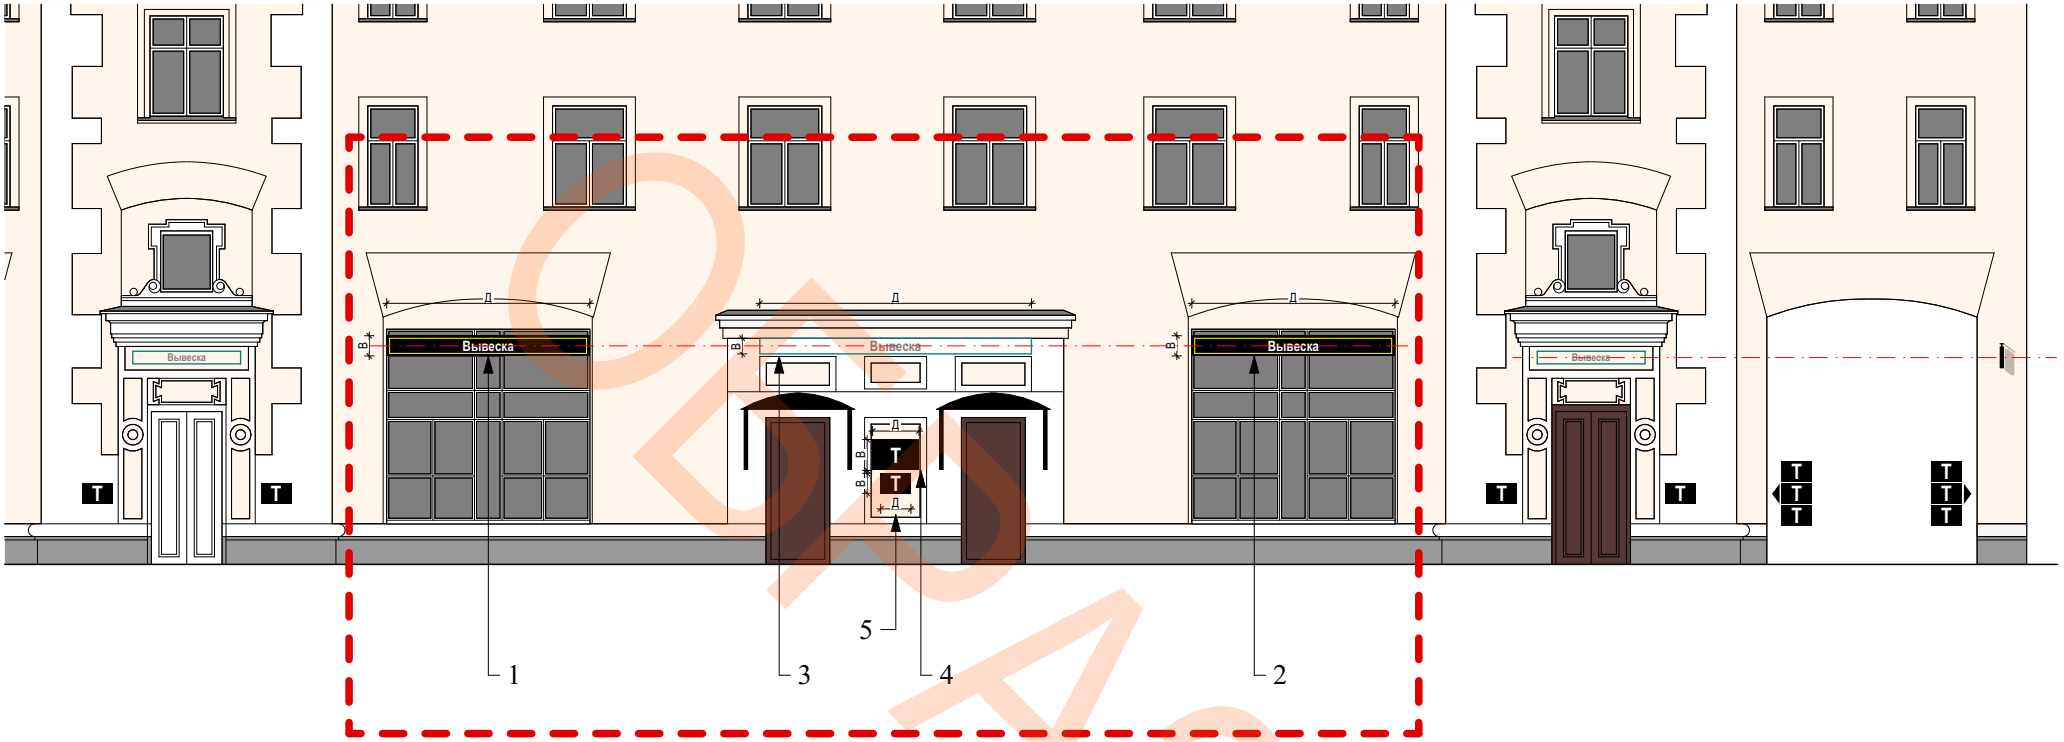

ОБРАЗЕЦ

ЭКСПЛИКАЦИЯ ИНФОРМАЦИОННЫХ КОНСТРУКЦИЙ

№	Обозначение	Габаритные размеры (ДхВхШ) мм.	Тип конструкции	Вид конструкции Способ, тип освещения	Расстояние от плоскости фасада до края вывески. (мм.)
1-2	Вывеска	Д х В х Ш	Витринная	Объемные буквы и знаки с внутренним подсветом на подложке	———
3	Вывеска	Д х В х Ш	Настенная	Объемные буквы и знаки с внутренним подсветом без подложки	Э
4	Т	Д х В х Ш	Настенная	Информационная табличка	———
5	Т	Д х В х Ш	Настенная	Информационная табличка	———

				Заказчик:
				Объект:
				Адрес:
Должность	Фамилия	Подпись	Дата	
Архитектор				Дизайн-проект размещения информационных конструкций
				Стадия: П; Лист: 06; Листов: 08
				Чертеж фасадов и места размещения. Указывается масштаб разрабатываемого чертежа: (М 1:50; М 1:100; М 1:200)
				Исполнитель

* Информационные конструкции должны иметь сквозную нумерацию

СХЕМА КРЕПЛЕНИЯ ИНФОРМАЦИОННОЙ КОНСТРУКЦИИ

Схема крепления информационной конструкции
объемные буквы и знаки без подложки


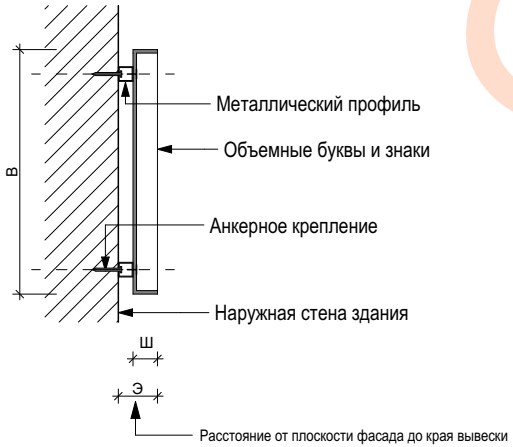



Схема крепления витринной информационной конструкции
объемные буквы и знаки на подложке

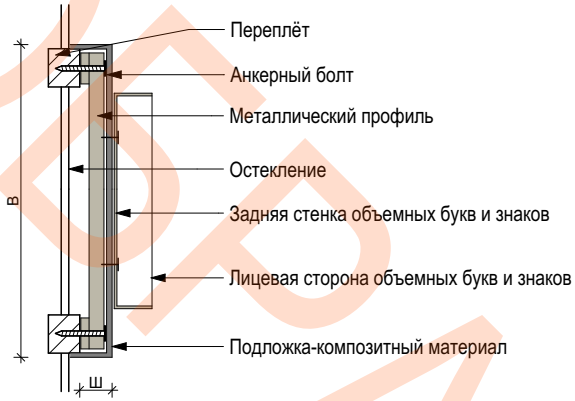


Для объектов культурного наследия

При размещении информационных конструкций на **объектах культурного наследия**, графическая врисовка включает изображение информационного поля конструкции (буквы, буквенные символы, аббревиатура, цифры), декоративно-художественных элементов - логотипов, знаков и т.д..
Колористическое решение конструкций и схему крепления на фасаде.

Например: при наличии декаративно-художественных элементов.

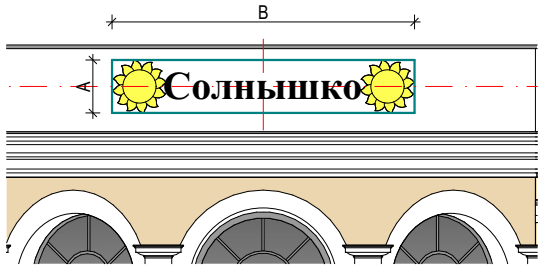


Например: при отсутствии декаративно-художественных элементов.

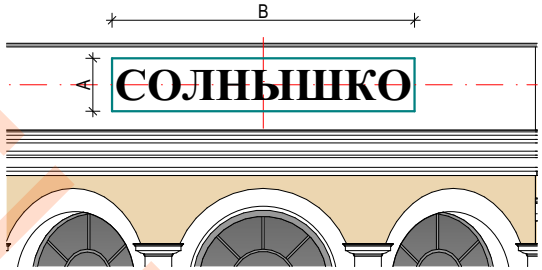

ОБРАЗЕЦ

				Заказчик:		
				Объект:		
Должность	Фамилия	Подпись	Дата	Адрес:		
Архитектор				Дизайн-проект размещения информационных конструкций	Стадия	Лист / Листов
					П	07 / 08
				Схема крепления информационной конструкции	Исполнитель	

ФОТОМОНТАЖ. ВИД 1

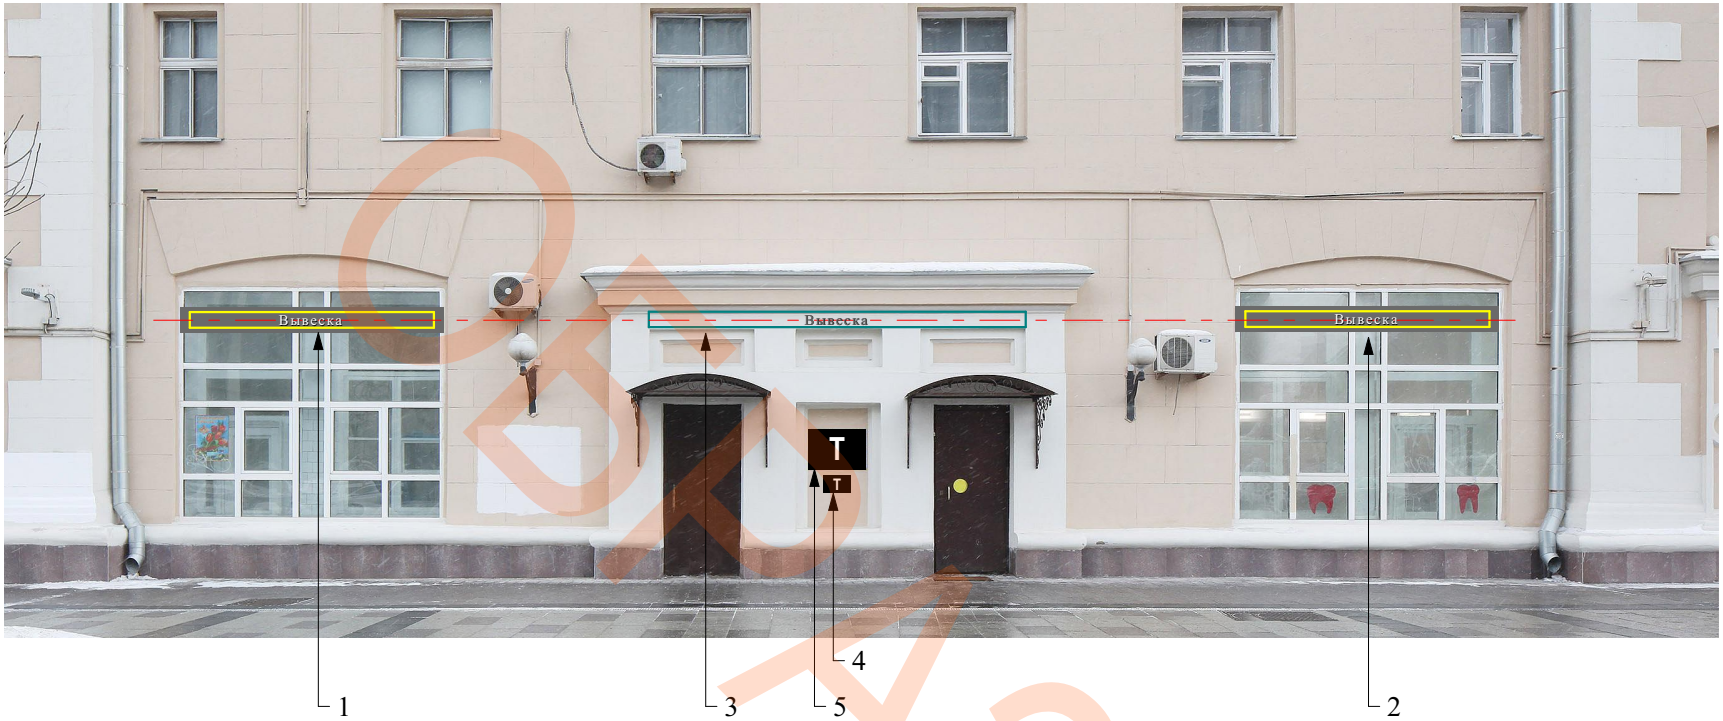

ЭКСПЛИКАЦИЯ ИНФОРМАЦИОННЫХ КОНСТРУКЦИЙ

№	Обозначение	Габаритные размеры (ДхВхШ) мм.	Тип конструкции	Вид конструкции Способ, тип освещения	Расстояние от плоскости фасада до края вывески. (мм.)
1-2	Вывеска	Д х В х Ш	Витринная	Объемные буквы и знаки с внутренним подсветом на подложке	———
3	Вывеска	Д х В х Ш	Настенная	Объемные буквы и знаки с внутренним подсветом без подложки	Э
4	Т	Д х В х Ш	Настенная	Информационная табличка	———
5	Т	Д х В х Ш	Настенная	Информационная табличка	———

* Фотомонтаж должен обеспечить в полном объеме четкую демонстрацию предполагаемого места размещения вывески и всех иных конструкций, размещенных на всех внешних поверхностей здания,а также не содержать иных объектов припятствующих указанной демонстрации, в том числе автомобильный транспорт.
Фотографии должны быть выполнены на момент подачи запроса о предоставлении государственной услуги.

Должность	Фамилия	Подпись	Дата
Архитектор			

Заказчик:
Объект:
Адрес:

Дизайн-проект размещения информационных конструкций	Стадия	Лист	Листов
	П	08	08
Фотомонтаж. Вид 1	Исполнитель		

ОБРАЗЕЦ